
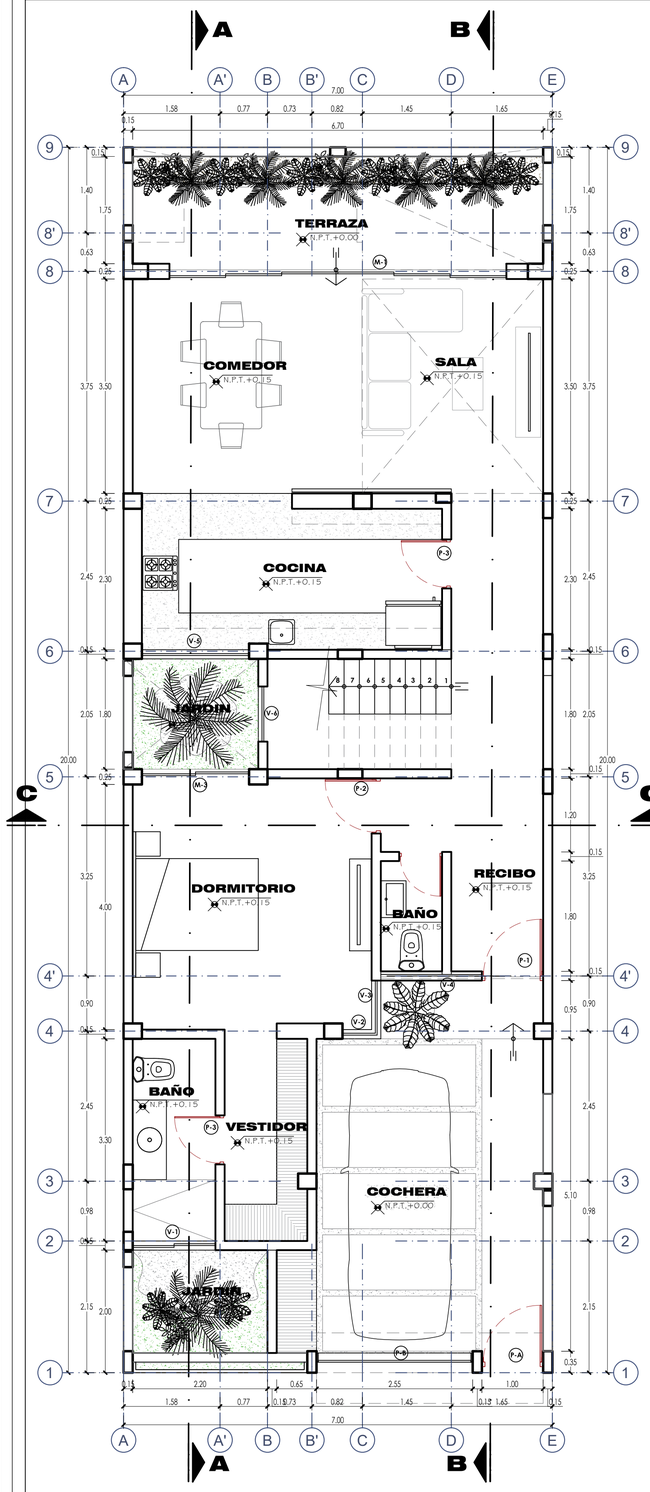



PLANTA PRIMER PISO

Esc: 1/50

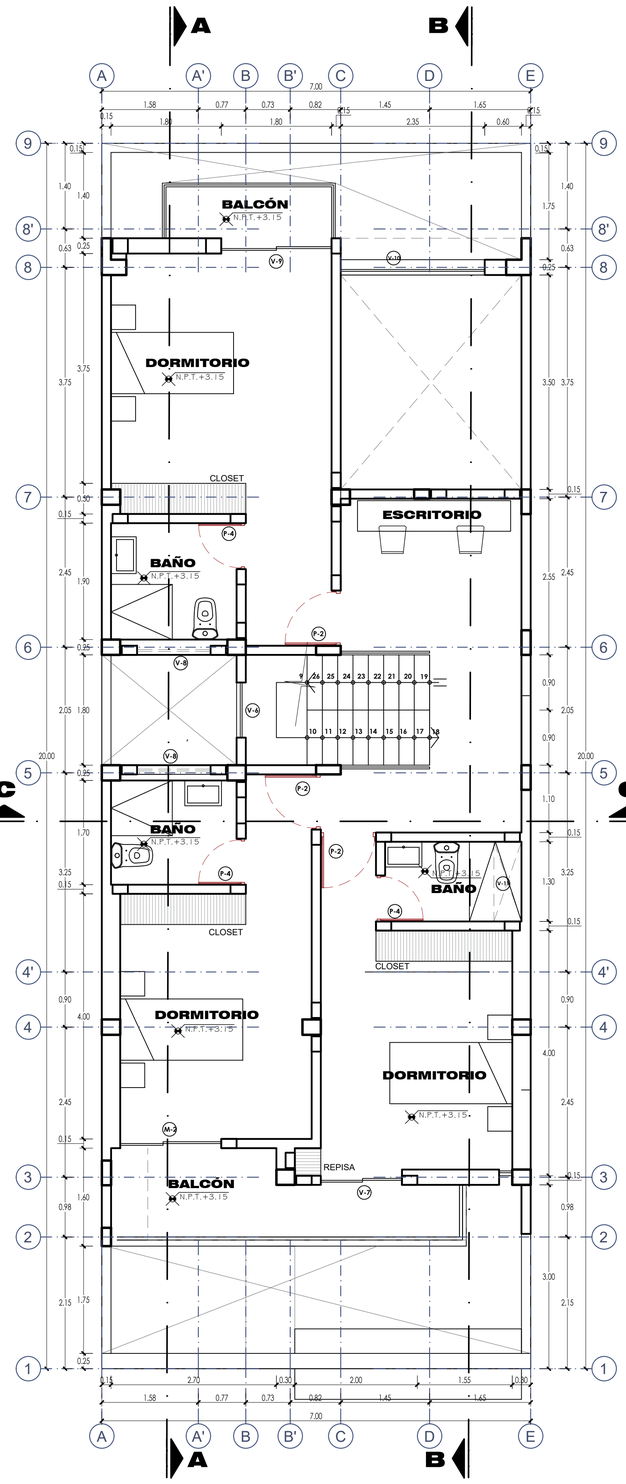


PLANTA SEGUNDO PISO

Esc: 1/50

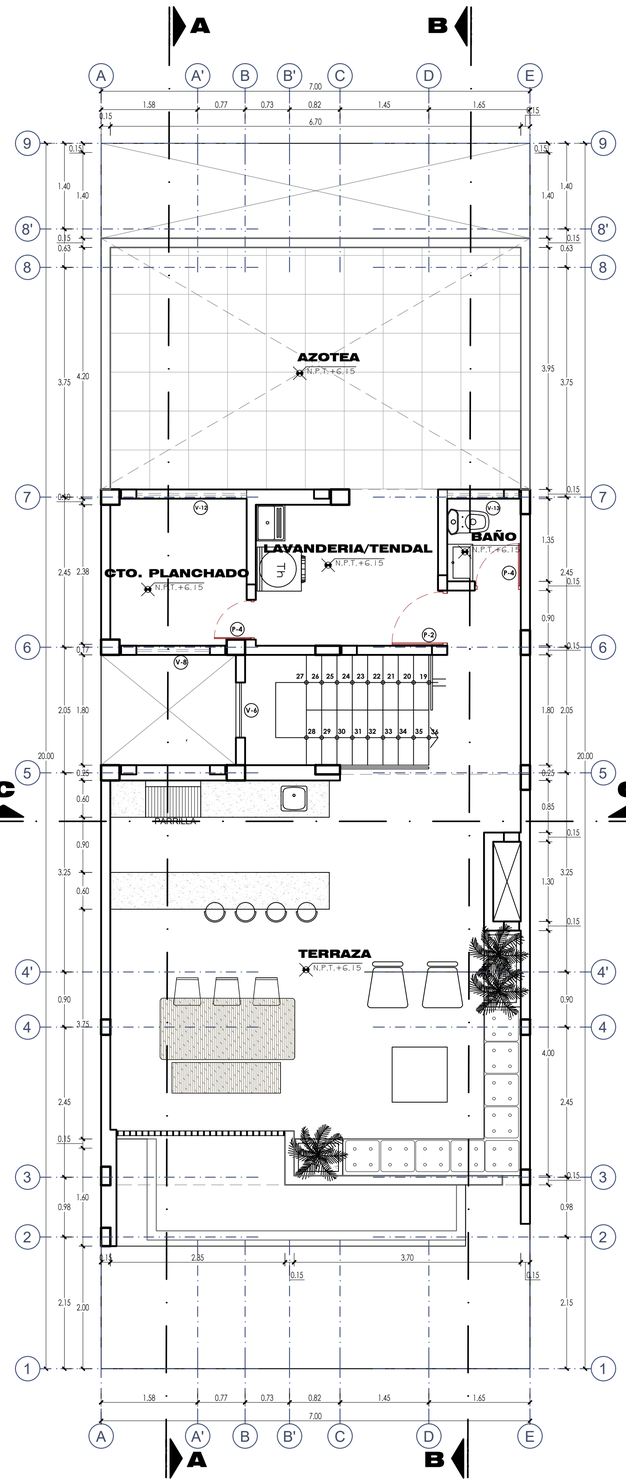

PLANTA AZOTEA

Esc: 1/50

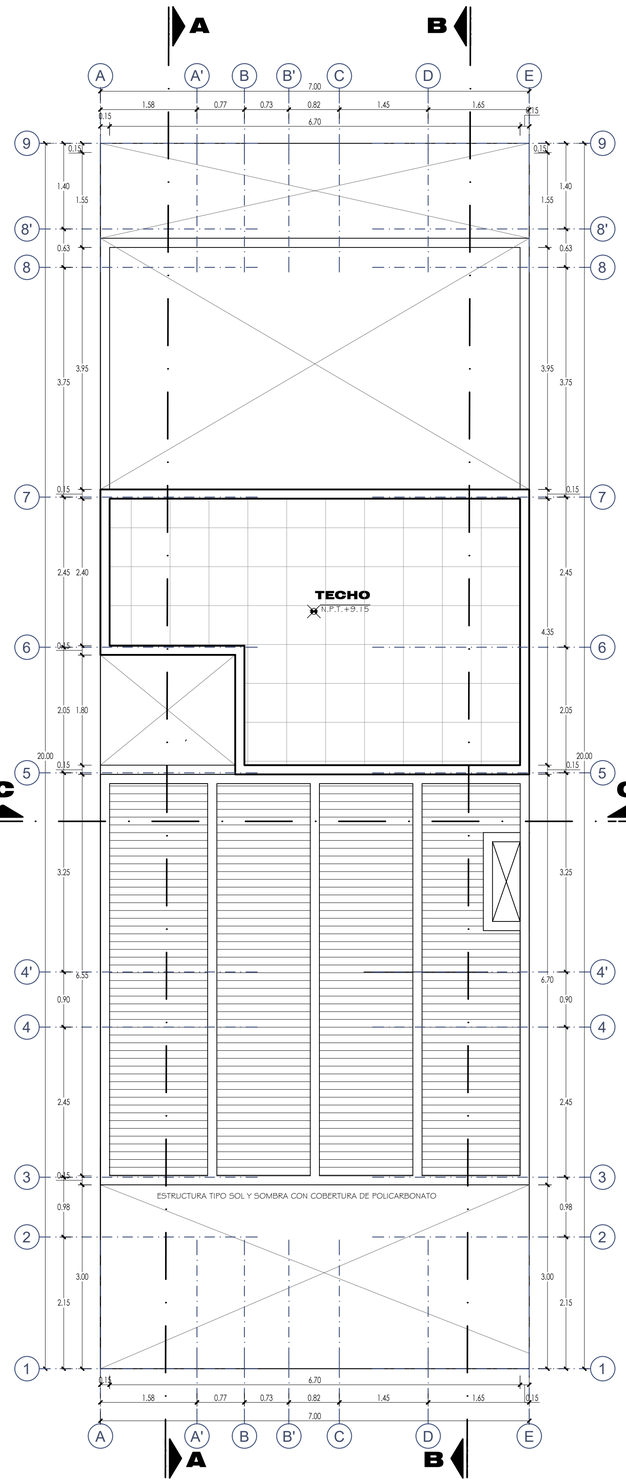

PLANTA TECHO

Esc: 1/50

PROYECTO: VIVIENDA UNIFAMILIAR	UBICACIÓN : URB. MIRAFLORES BOULEVARD PARK PLAZA Mz. AN - Lote 18 - II ETAPA - CASTILLA PROPIETARIO : Sra. ROSSEMERY YANIRE FERNÁNDEZ ROJAS DNI: 80366589	DIBUJO : JLAY RESPONSABLE : ARQ. RENZO IZQUIERDO ESCALA : 1 / 50 FECHA : JULIO 2026	TITULO DE LÁMINA: ARQUITECTURA PLANTAS DE DISTRIBUCIÓN 1er, 2do PISO, AZOTEA Y TECHO	N° LÁMINA: A-01




SECCIÓN A - A

Esc: 1/50



SECCIÓN B - B

Esc: 1/50

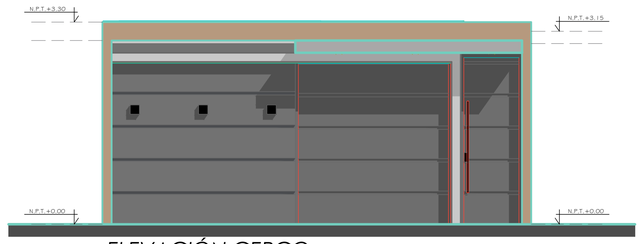

ELEVACIÓN CERCO

Esc: 1/50





SECCIÓN C - C

Esc: 1/50

CUADRO DE VANOS - PUERTAS

TIPO	ANCHO	ALTO	ALFEIZER	AMBIENTE
P-A	1.00	2.80	----	INGRESO EXTERIOR PRINCIPAL
P-B	2.55	2.65	----	COCHERA
P-1	1.00	2.10	----	INGRESO INTERIOR PRINCIPAL
P-2	0.90	2.10	----	INGRESO DORMITORIOS
P-3	0.80	2.10	----	BAÑO
P-4	0.75	2.10	----	BAÑO

CUADRO DE VANOS - MAMPARA

TIPO	ANCHO	ALTO	ALFEIZER	AMBIENTE
M-1	5.50	2.60	----	SALA - COMEDOR
M-2	1.65	2.80	----	DORMITORIO 03
M-3	2.80	1.75	----	DORMITORIO 01

CUADRO DE VANOS - VENTANAS

TIPO	ANCHO	ALTO	ALFEIZER	AMBIENTE
V-1	2.65	1.35	-----	BAÑO
V-2	0.65	2.80	-----	DORMITORIO 01
V-3	0.95	2.80	-----	BAÑO
V-4	0.60	2.65	2.20	BAÑO / RECIBO
V-5	1.80	1.75	1.00	COCINA
V-6	2.80	0.90	-----	ESCALERA
V-7	1.80	1.55	1.00	DORMITORIO 03
V-8	0.60	1.20	2.20	BAÑO
V-9	1.80	1.80	1.00	DORMITORIO 04
V-10	1.80	2.35	1.00	SALA
V-11	0.60	1.30	2.20	BAÑO
V-12	0.60	1.80	2.20	CTO. PLANCHAR
V-13	0.60	1.20	2.20	BAÑO

PROYECTO: VIVIENDA UNIFAMILIAR	UBICACIÓN : URB. MIRAFLORES BOULEVARD PARK PLAZA Mz. AN - Lote 18 - II ETAPA - CASTILLA PROPIETARIO : Sra. ROSSEMERY YANIRE FERNÁNDEZ ROJAS DNI: 80366589	DIBUJO : JLAY RESPONSABLE : ARQ. RENZO IZQUIERDO ESCALA : 1 / 50 FECHA : JULIO 2026	TITULO DE LÁMINA: ARQUITECTURA SECCIONES Y ELEVACIONES	N° LÁMINA: A-02